



SIDE ELEVATION / STRINGER PROFILE

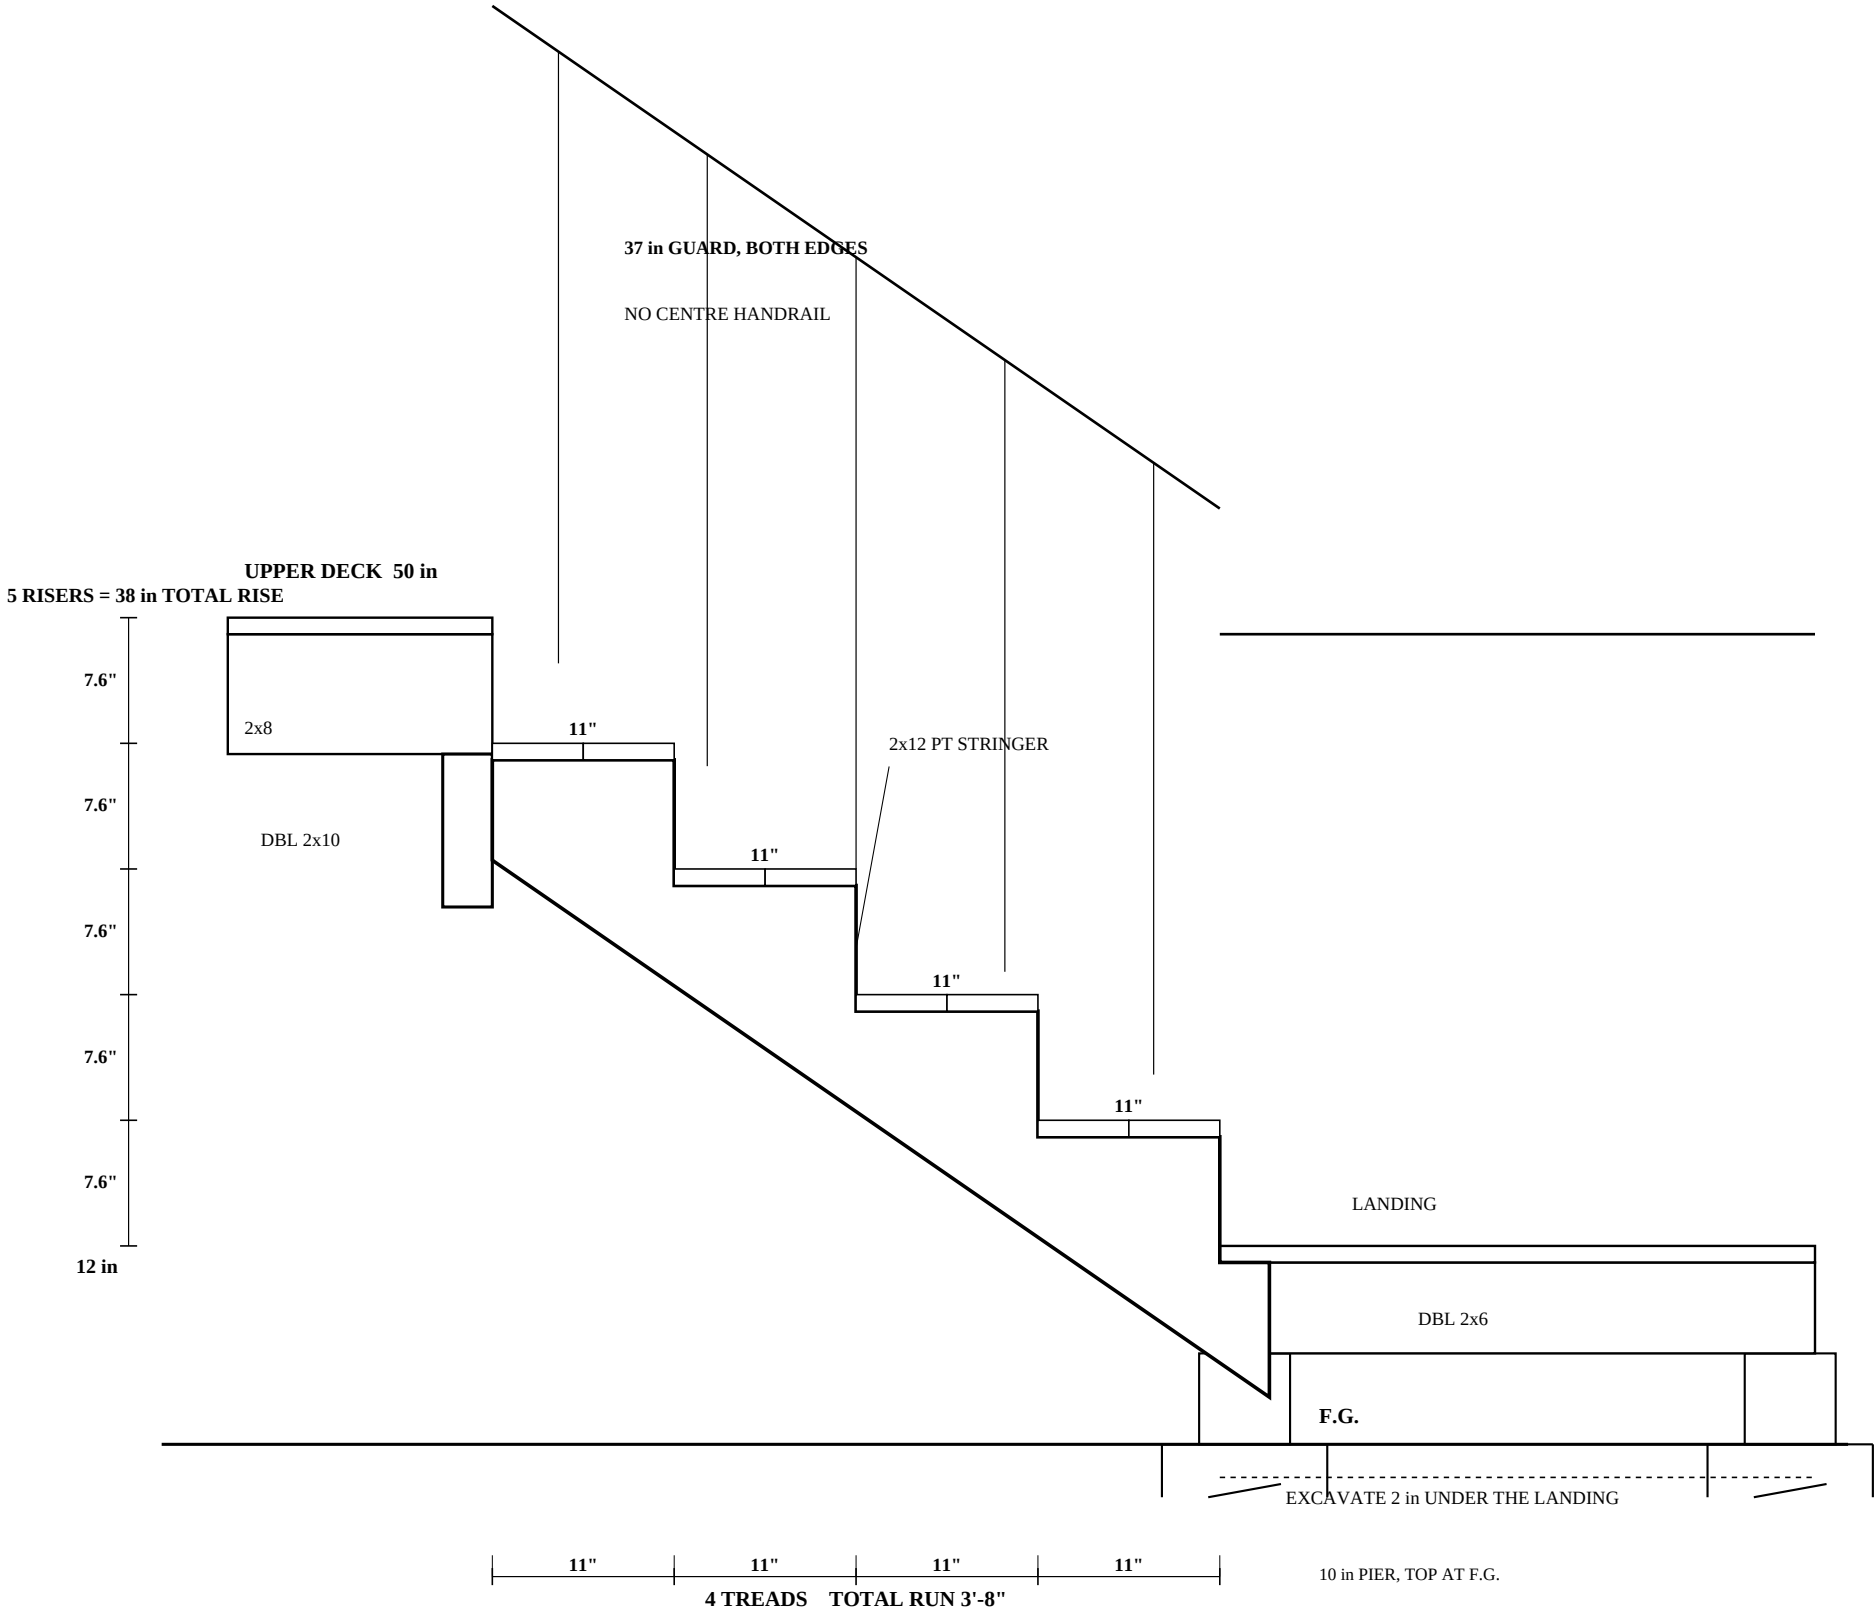


LAYOUT

2x12 throat after the cuts: 5.00 in. Two 5/4x6 boards on each tread.
If the surfaces change the 38 in rise, recalculate before cutting. Connector not selected.
OBC 2024 private stair: rise 125–200 mm, run 255–355 mm. This flight is inside both.
Prepared in accordance with the 2024 Ontario Building Code and applicable Municipality of North Grenville zoning, pool-enclosure and permit requirements. Final construction is subject to municipal review and approval, field verification, and all conditions of the issued permit.


STRINGER AND LANDING PLAN

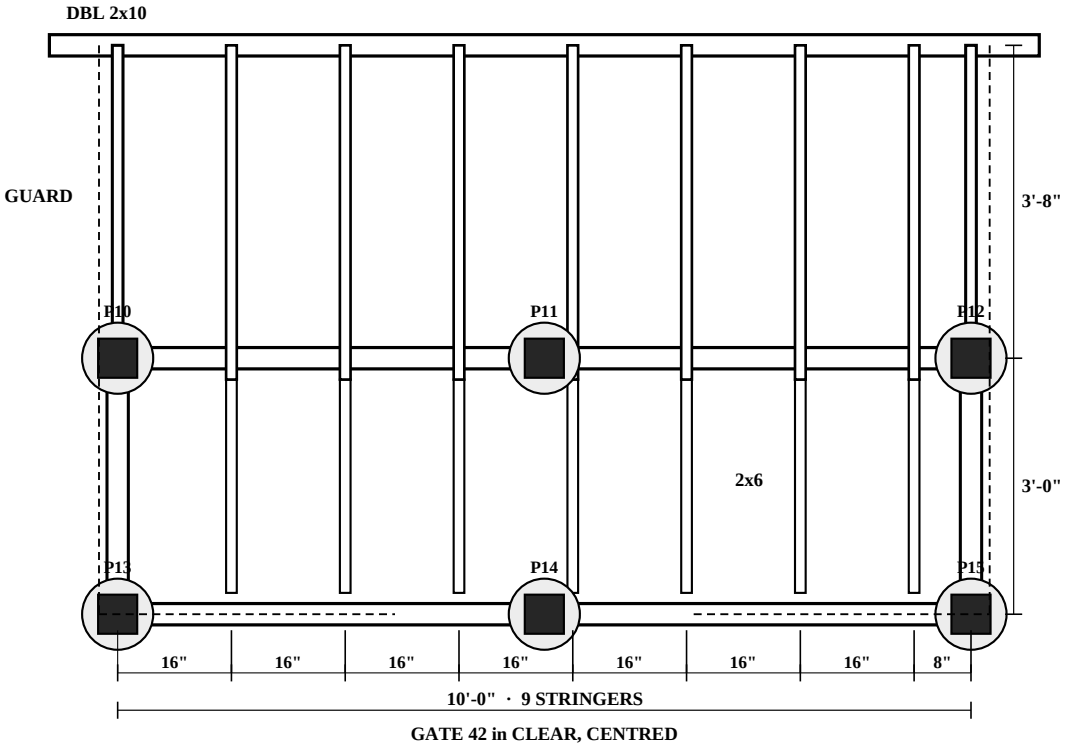

TOP — PLUMB CUT ON THE DBL 2x10

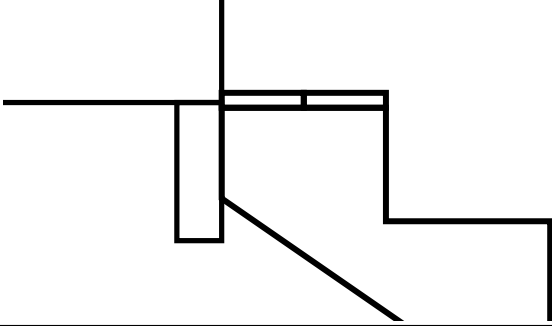

BOTTOM — 3 in SEAT ON THE DBL 2x6

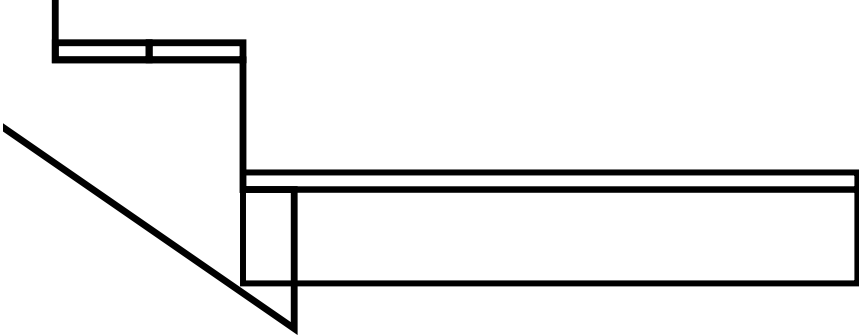

LINDA BUSHEL — STAIR AND LOWER LANDING

CONSTRUCTION DRAWING CAPABILITY TEST — JOEL REVIEW — NOT FINAL

D'Arcy's Way, Kemptville, ON K0G 1J0

Brayman Construction Inc., 411 St. John Street
Merrickville, ON K0G 1N0
Profile 6.2 pt = 1 in. Plan 34 pt = 1 ft.
Same geometry as CT-1. Not a separate stair design.

CT-2 STAIR

29 Sep 2026
11 x 17 in
Not a permit. Not a seal.