




SIDE ELEVATION / STRINGER PROFILE

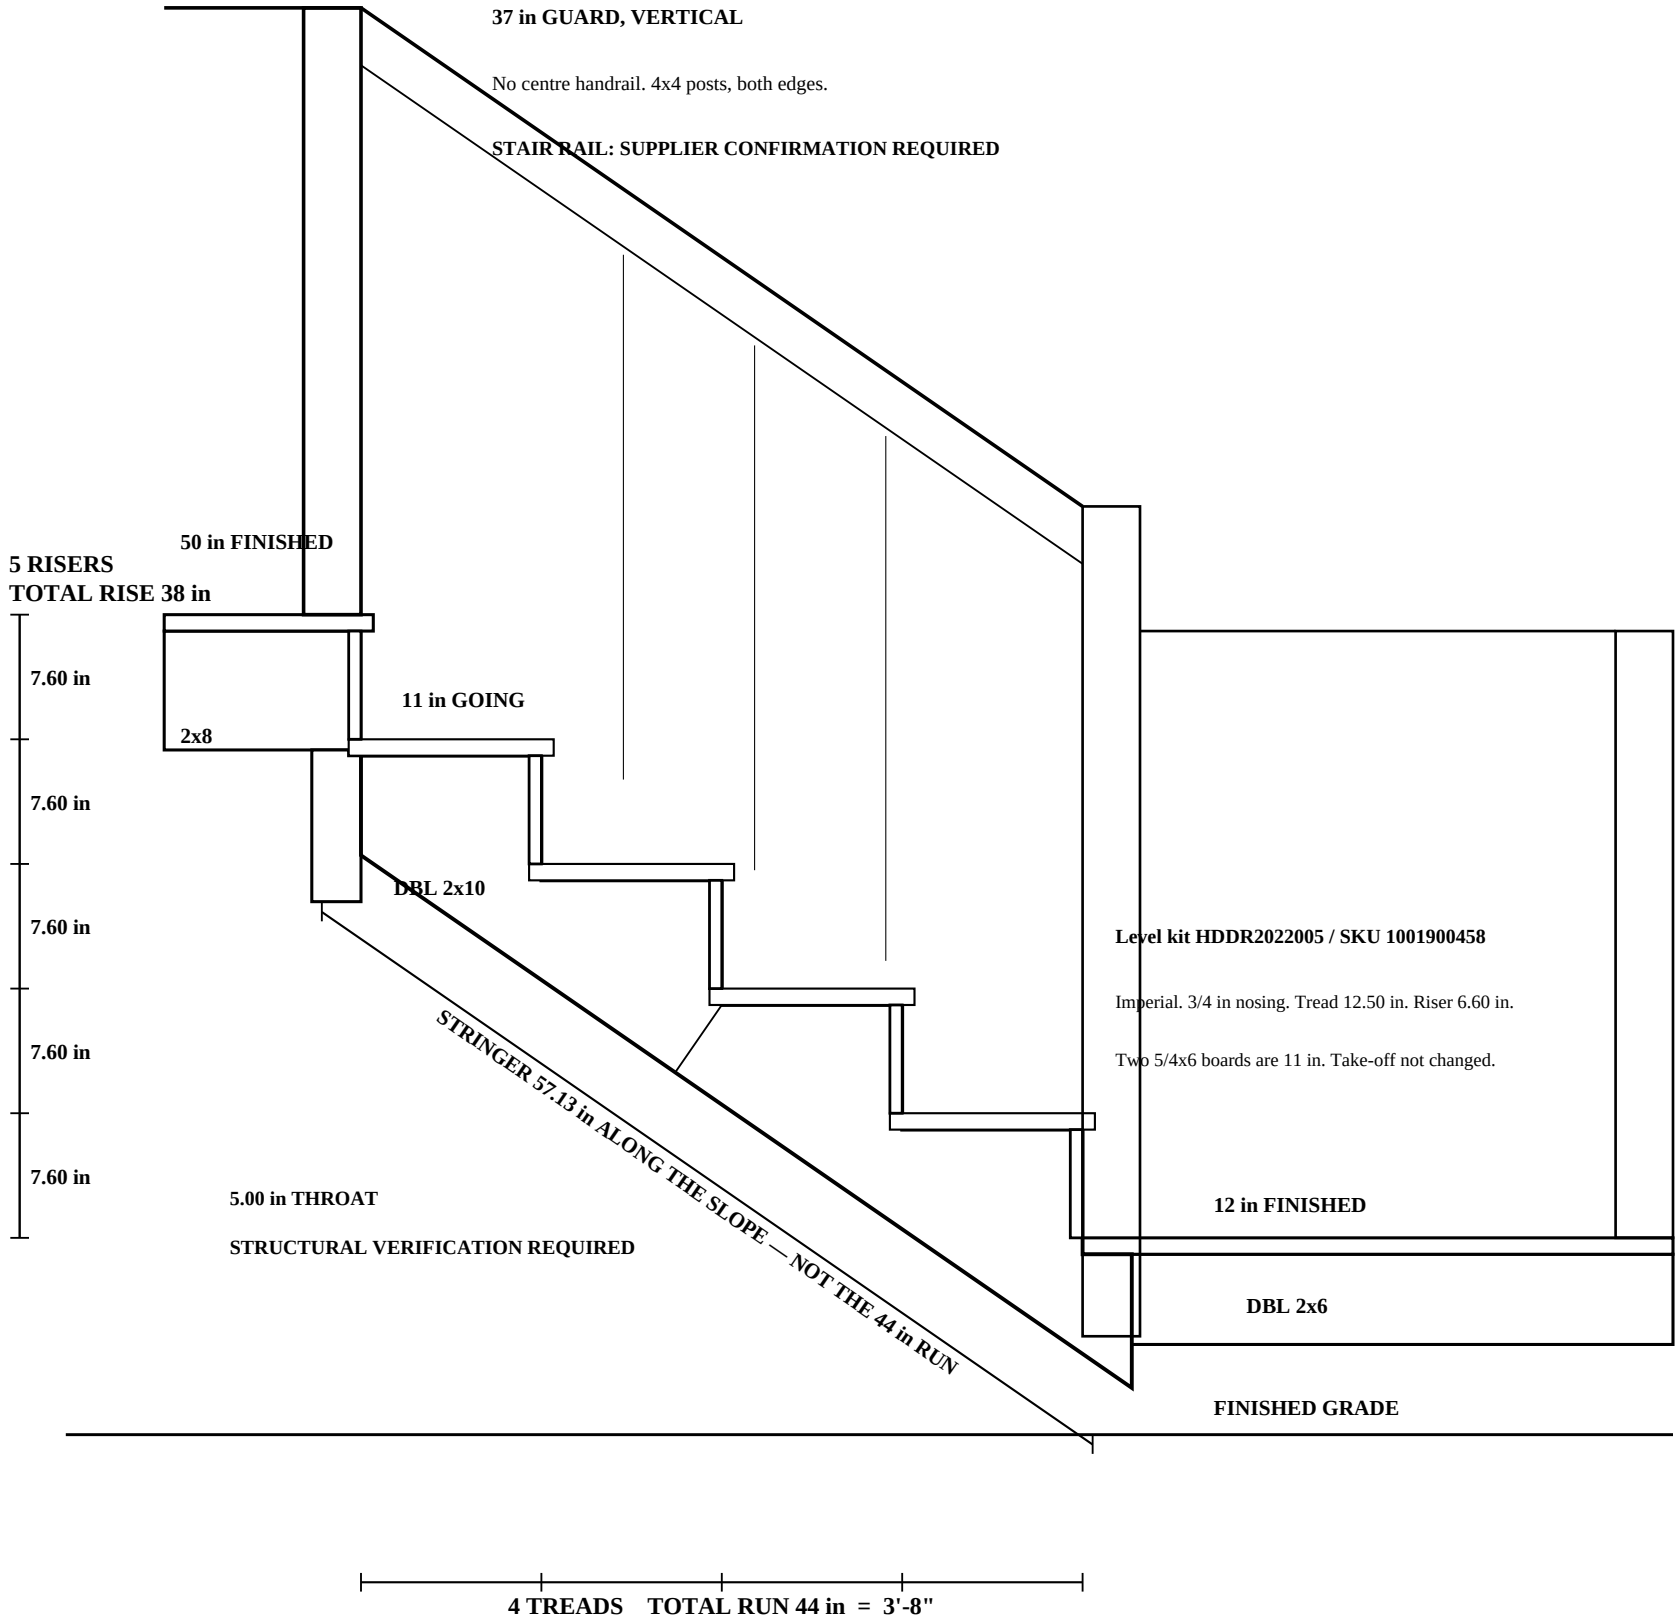

STRINGER, GUARD, AND LANDING PLAN

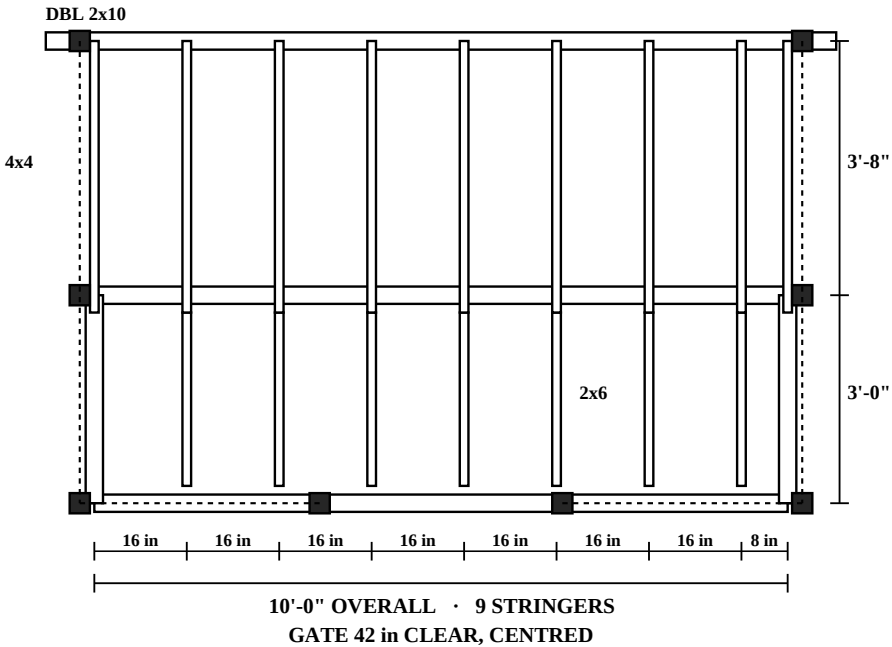


TOP CONNECTION · 8 pt = 1 in · 2x12 TO DBL 2x10

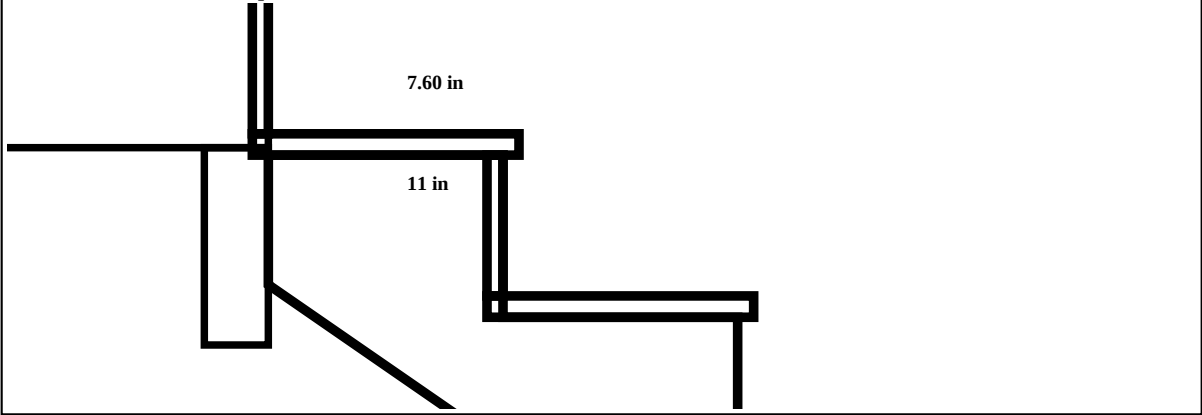

HARDWARE NOT SELECTED. EXTERIOR-RATED. PT-COMPATIBLE.

BOTTOM BEARING · 8 pt = 1 in · SEAT ON DBL 2x6

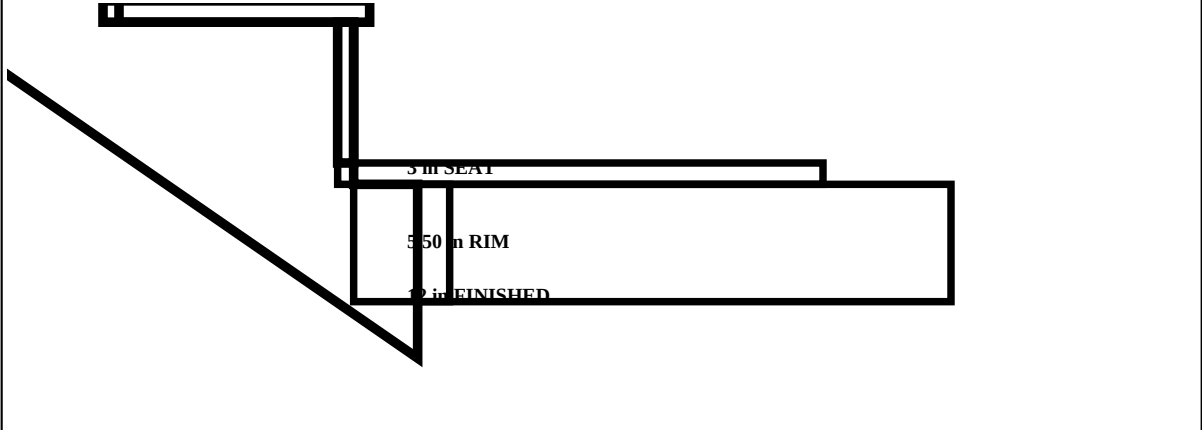

Prepared in accordance with the 2024 Ontario Building Code and applicable Municipality of North Grenville zoning, pool-enclosure and permit requirements. Final construction is subject to municipal review and approval, field verification, and all conditions of the issued permit.

LINDA BUSHEL — STAIR AND LOWER LANDING

CT-2 REFINEMENT — JOEL REVIEW — NOT FINAL

D'Arcy's Way, Kemptville, ON K0G 1J0

Brayman Construction Inc., 411 St. John Street

Merrickville, ON K0G 1N0

Same geometry as CT-1 and the first CT-2 proof.

Profile 6.15 pt = 1 in. Plan 26 pt = 1 ft.

CT-2 R2

29 Sep 2026

11 x 17 in

Not a permit. Not a seal.