


PLAN

3 in = 1 ft

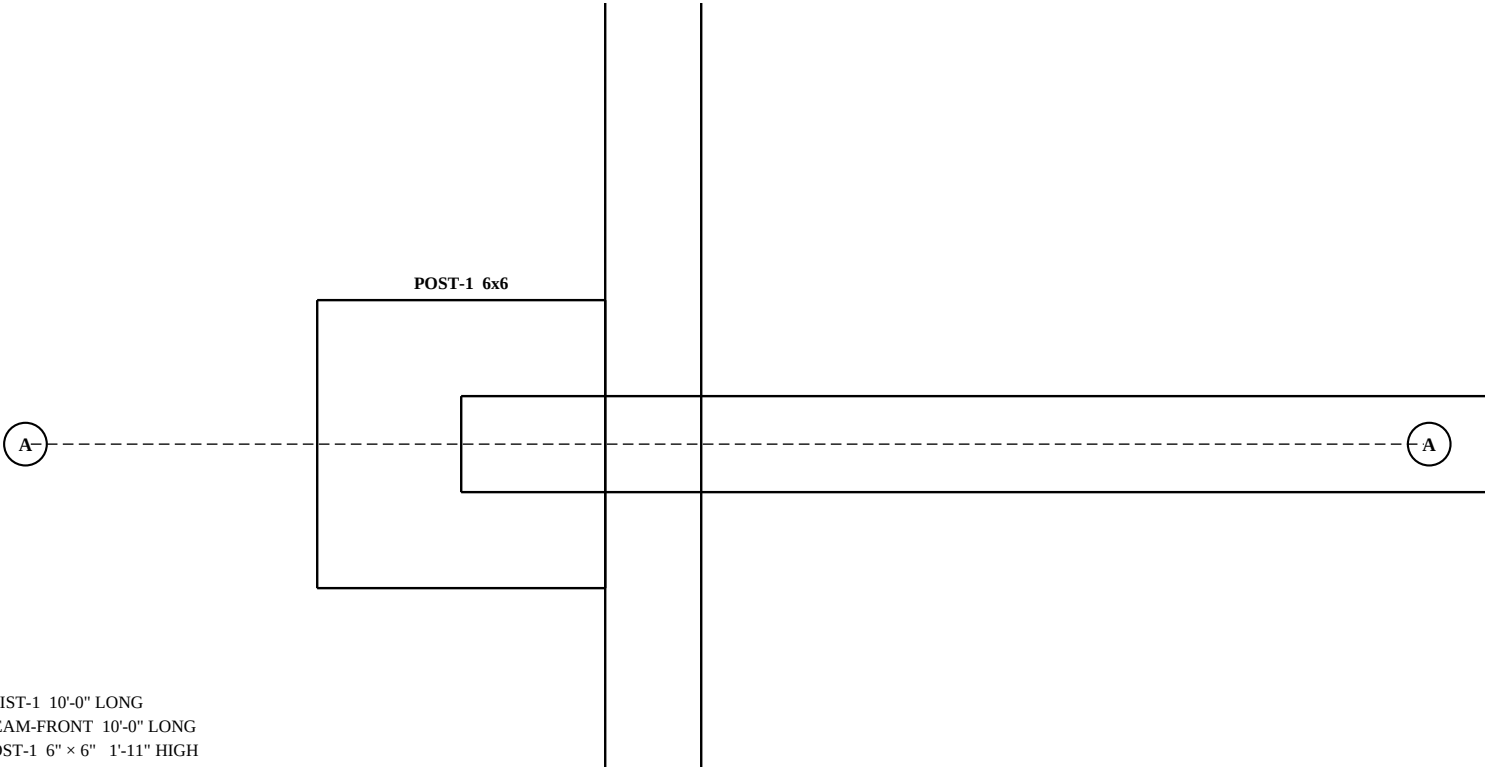


FRONT ELEVATION

1 1/2 in = 1 ft




SECTION A

1 1/2 in = 1 ft

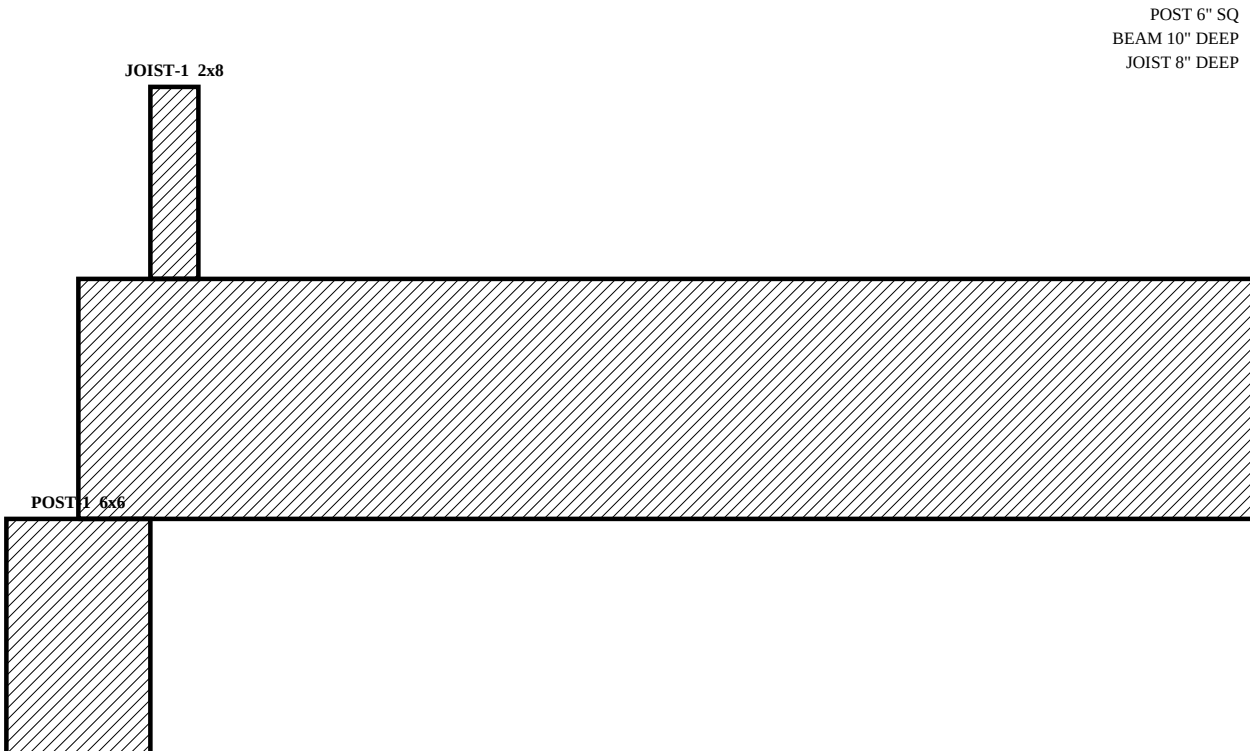

DETAIL 1 POST / BEAM

3 in = 1 ft

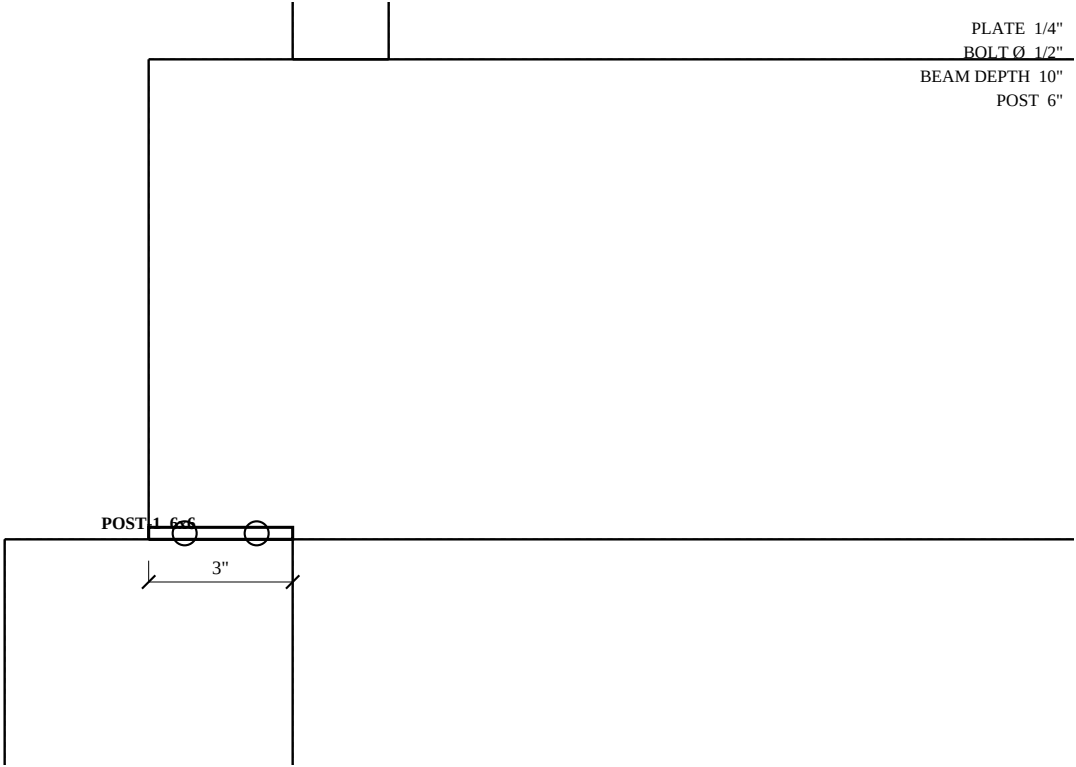

NOTES

1. POST-1 BEARS ON BEAM-FRONT. rel-bear-post-1-beam-front.
2. BEAM-FRONT SUPPORTS JOIST-1. rel-9.
3. fixture post cap. fixture bolt × 2. Fixture plate thickness is nominal.
4. Profiles and positions are the stored model. Overlap is not support.

Brayman Construction

COMPLETE DECK DRAWING ENGINE FIXTURE

POST, BEAM, AND JOIST

SHEET 1 REV A 2026-10-02

SCALE AS NOTED

PRELIMINARY CONSTRUCTION DRAWING — SUBJECT TO PERMIT REVIEW AND FIELD VERIFICATION